
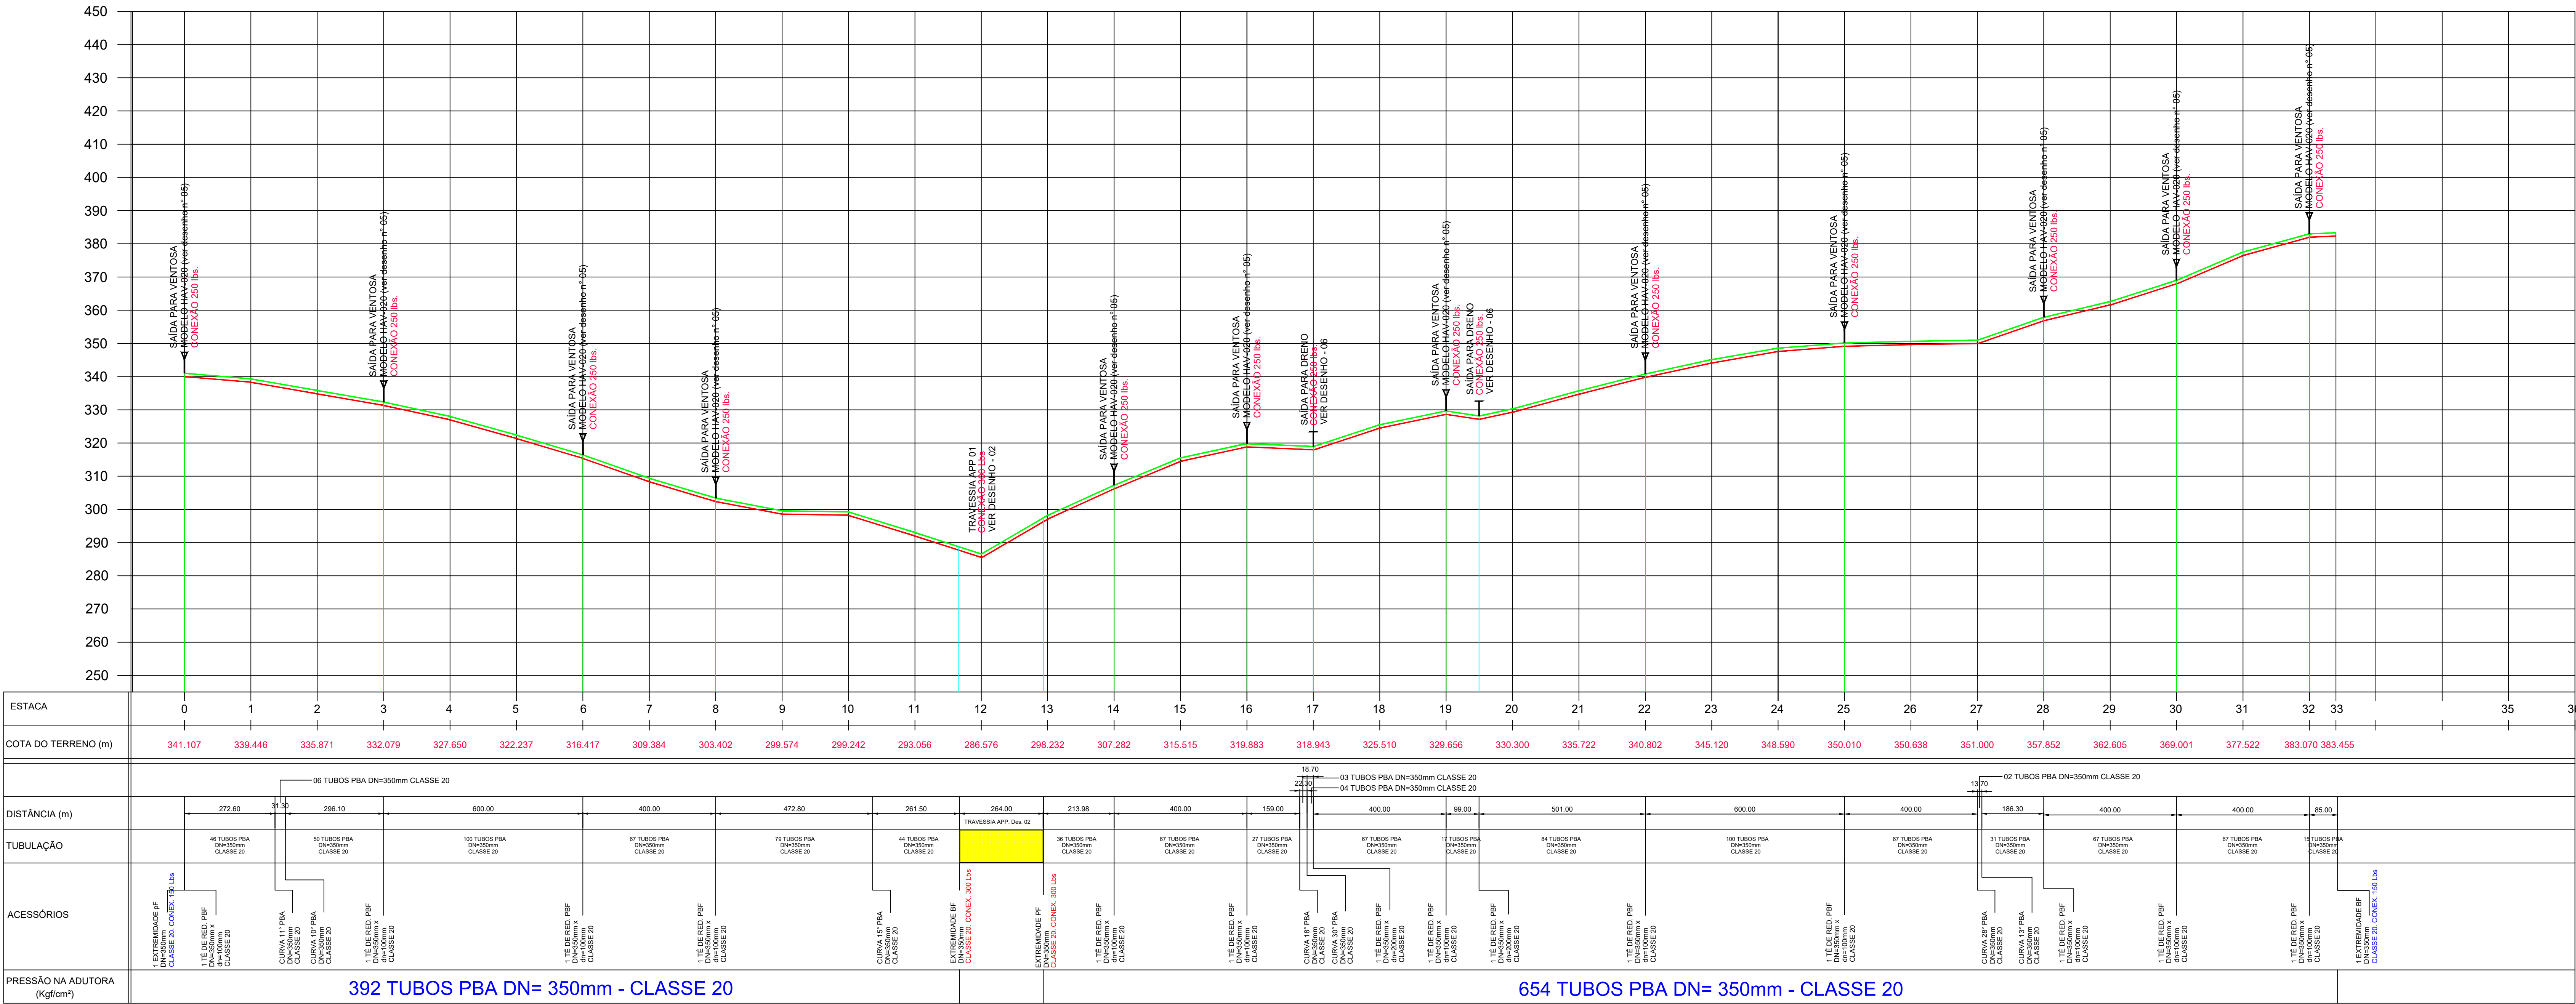


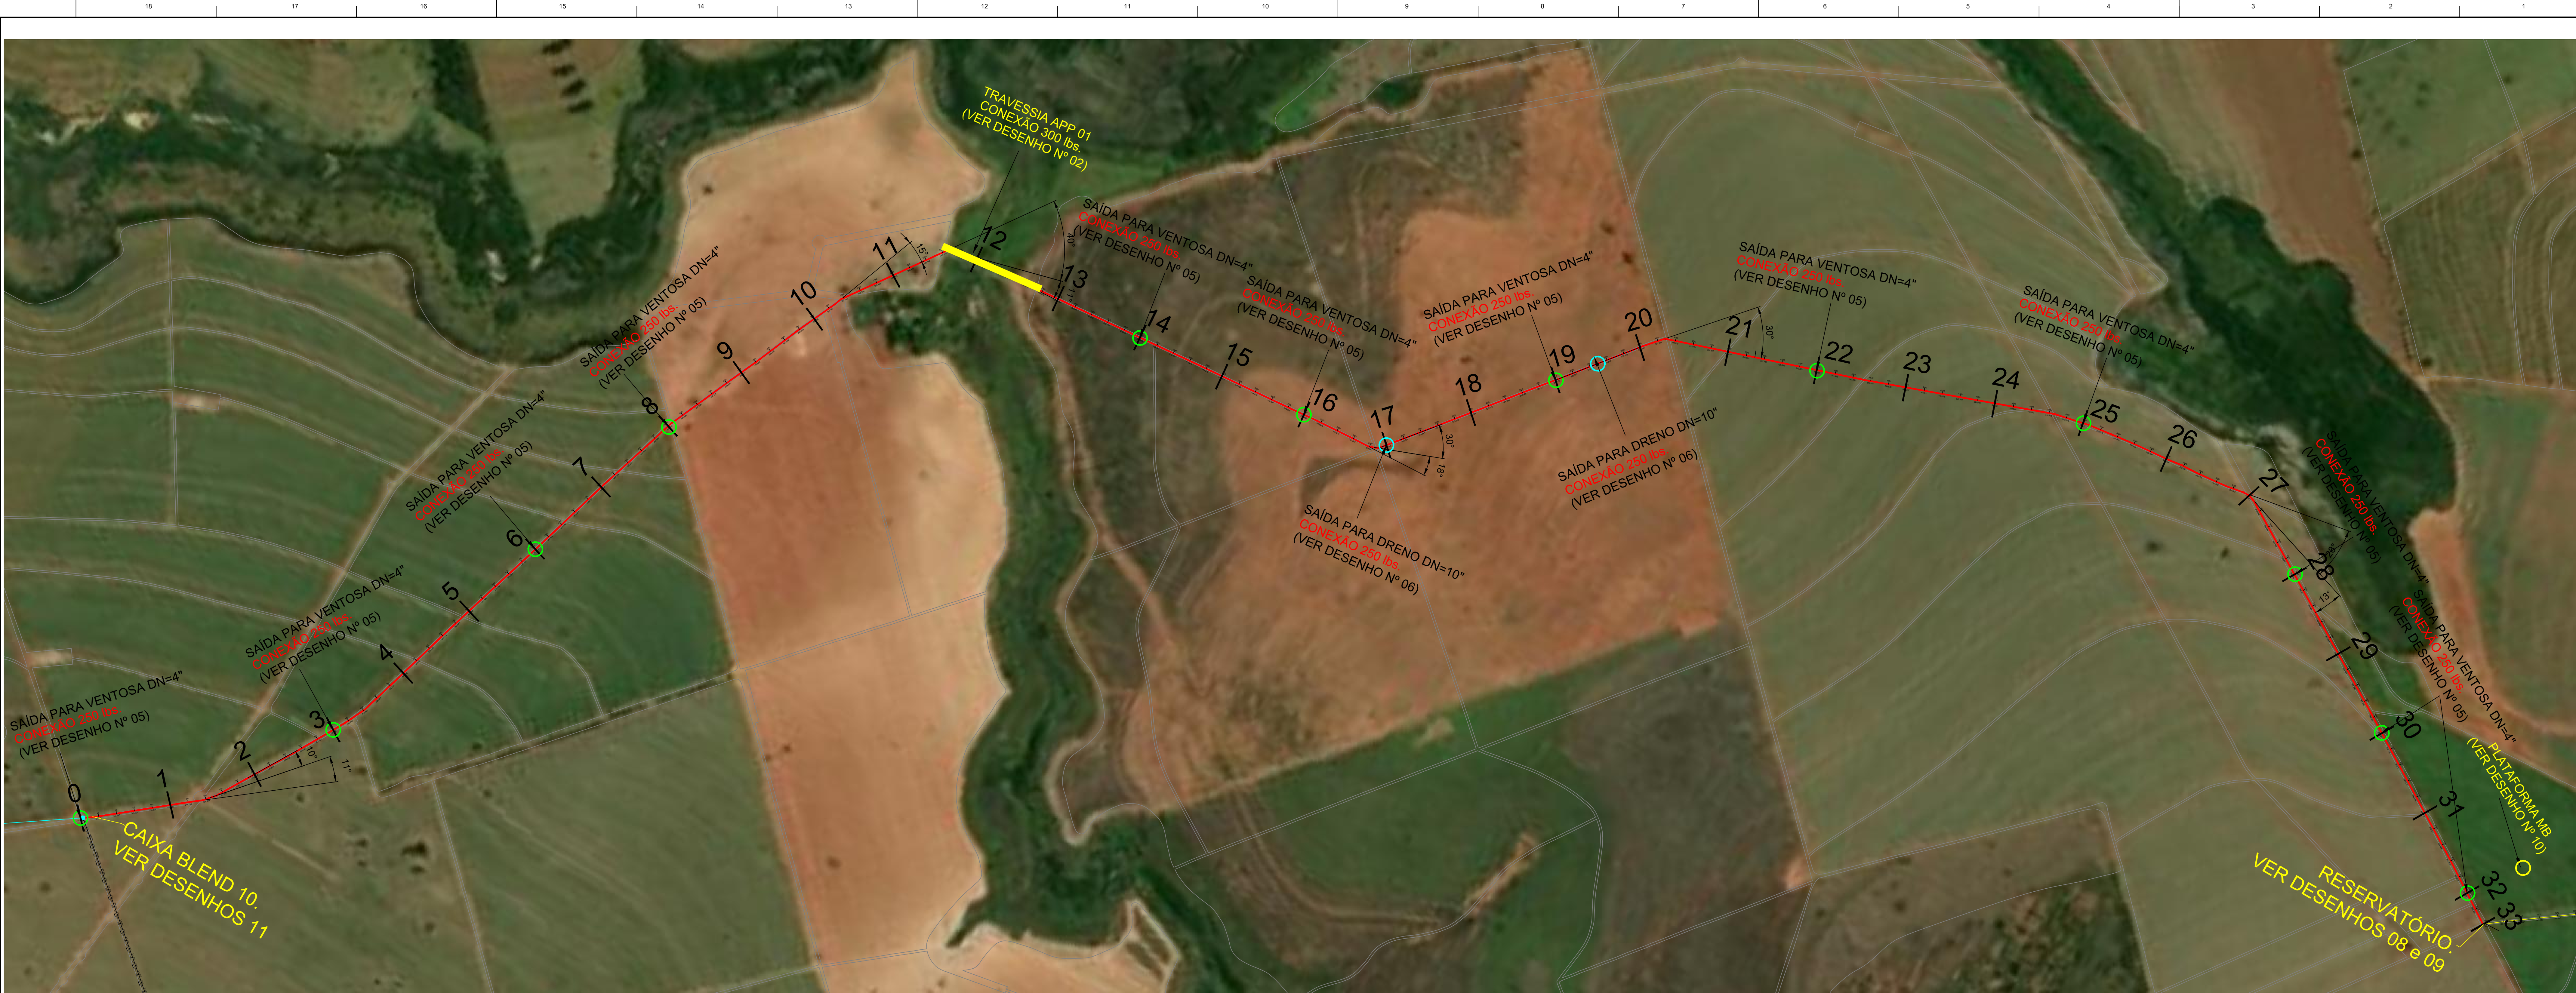

DETALHE: BLOCOS DE ANCORAGEM				
BLOCOS DE ANCORAGEM NA ADUTORA				
PIÇA	ANGULO	DIAMETRO	ESTACA	POSICAO
CURVA	11	350	Entre 01 e 02	Horizontal
CURVA	15	350	Entre 10 e 11	Horizontal
CURVA	18	350	Entre 16 e 17	Horizontal
CURVA	30	350	Entre 16 e 17	Horizontal
CURVA	30	350	Entre 20 e 21	Horizontal
CURVA	28	350	Entre 27 e 28	Horizontal
CURVA	13	350	Entre 27 e 28	Horizontal
CURVA	90	350	Entre 32 e 33	Horizontal
TE	VENTOSA (Ver detalhes e dimensões nos desenhos específicos)			
VÁLVULAS	(Ver detalhes e dimensões nos desenhos específicos)			
FINAL	(Ver detalhes e dimensões nos desenhos específicos)			

AS TRAVESSIAS DE CARREADOR COM TRAFEGO, DEVEM SER PROTEGIDAS COM PLACAS DE CONCRETO. VER DESENHO DA VALA, DESENHO 04.

- NOTAS:
- 1) PROJETO ELABORADO COM BASE EM LEVANTAMENTOS TOPOGRÁFICOS FORNECIDOS PELO CLIENTE.
 - 2) HAV-229: VÁLVULA VENTOSA SECA (ESTANQUE) COMBINADA TRIPLICE FUNÇÃO, PARA VINHAÇA, CORPO TOTALMENTE EM AÇO INOX. FLUTUADOR INFERIOR EM AÇO INOX. FLUTUADOR SUPERIOR EM POLIPROPILENO EXPANDIDO, JUNTAS EM BUNA-N, VEDAÇÃO DO FLUTUADOR EM EPDM, PRESSÃO DE TRABALHO DE 0,2 A 16,0 KGf/cm², TEMPERATURA ATÉ 80°C, CONEXÃO FLANGEADA DE 3", NORMA ANSI B16.5. MODELO HAV-020 MARCA HIDRO-AMBIENTAL.
 - 3) EM LOCAIS DE TRAFEGO PESADO E INTENSO, A TUBULAÇÃO DEVERÁ SER PROTEGIDA COM LAJE DE CONCRETO ARMADO CONFORME DES. N° 04
 - 4) ESQUEMA DA VALA PARA ASSENTAMENTO DA TUBULAÇÃO VER DES. N° 04
 - 5) FURAÇÃO DOS FLANGES DE RPVC SEQUE A NORMA ANSI B16.5.

LISTA DE MATERIAL DA ADUTORA - RENASCER			
14	01	EXT PF, DN=350mm, CLASSE 20 AISI B 16.5 FURAÇÃO 3000 lbs	RPVC 60°C
13	01	EXT BF, DN=350mm, CLASSE 20 AISI B 16.5 FURAÇÃO 3000 lbs	RPVC 60°C
12	01	EXT BF, DN=350mm, CLASSE 20 AISI B 16.5 FURAÇÃO 150 lbs	RPVC 60°C
11	01	CURVA 90° PBA DN=350mm CLASSE 20 RIGIDEZ 3750Nm ²	RPVC 60°C
10	01	CURVA 13° PBA DN=350mm CLASSE 20 RIGIDEZ 3750Nm ²	RPVC 60°C
09	01	CURVA 20° PBA DN=350mm CLASSE 20 RIGIDEZ 3750Nm ²	RPVC 60°C
08	01	CURVA 20° PBA DN=350mm CLASSE 20 RIGIDEZ 3750Nm ²	RPVC 60°C
07	01	CURVA 16° PBA DN=350mm CLASSE 20 RIGIDEZ 3750Nm ²	RPVC 60°C
06	01	CURVA 15° PBA DN=350mm CLASSE 20 RIGIDEZ 3750Nm ²	RPVC 60°C
05	01	CURVA 11° PBA DN=350mm CLASSE 20 RIGIDEZ 3750Nm ²	RPVC 60°C
04	02	TE DE RED. PBF, DN=350 x 30=200mm, CLASSE 20 RIGIDEZ 150 lbs	RPVC 60°C
03	12	TE DE RED. PBF, DN=350 x 30=100mm, CLASSE 20 RIGIDEZ 150 lbs	RPVC 60°C
02	01	EXT PF, DN=350mm, CLASSE 20 AISI B 16.5 FURAÇÃO 150 lbs	RPVC 60°C
01	1050	TUBO PBA, DN= 350mm, CLASSE 20, BARRA 6m, RIGIDEZ 3.750Nm ²	RPVC 60°C
POS	QUANT		MATERIAL

Nº Rev	Data	Modificação	Revisor	Aprovação
DESENHO TIPO: ☐ PRELIMINAR ☒ P1 APROVAÇÃO ☐ CERTIFICADO				
DESENHO: ☐ APROVADO ☐ NÃO APROVADO ☐ APROVADO COM COMENTÁRIOS				
DATA: 11/05/2025				
RESPONSÁVEL: _____ DATA: _____				
VERONEZ PROJETOS E CONSULTORIA				
SANDOVALLINA - SP				
LOCAL: _____ DATA: _____				
DESCRIÇÃO: PROJETO DE FERTIRRIGAÇÃO - 2025				
ADUTORA DE RECALQUE - AR RENASCER				
PLANTA E PERFIL				
ESCALA: 1:10.000				
NÚMERO: SV-UMOE-PE-2501-01				
0				