
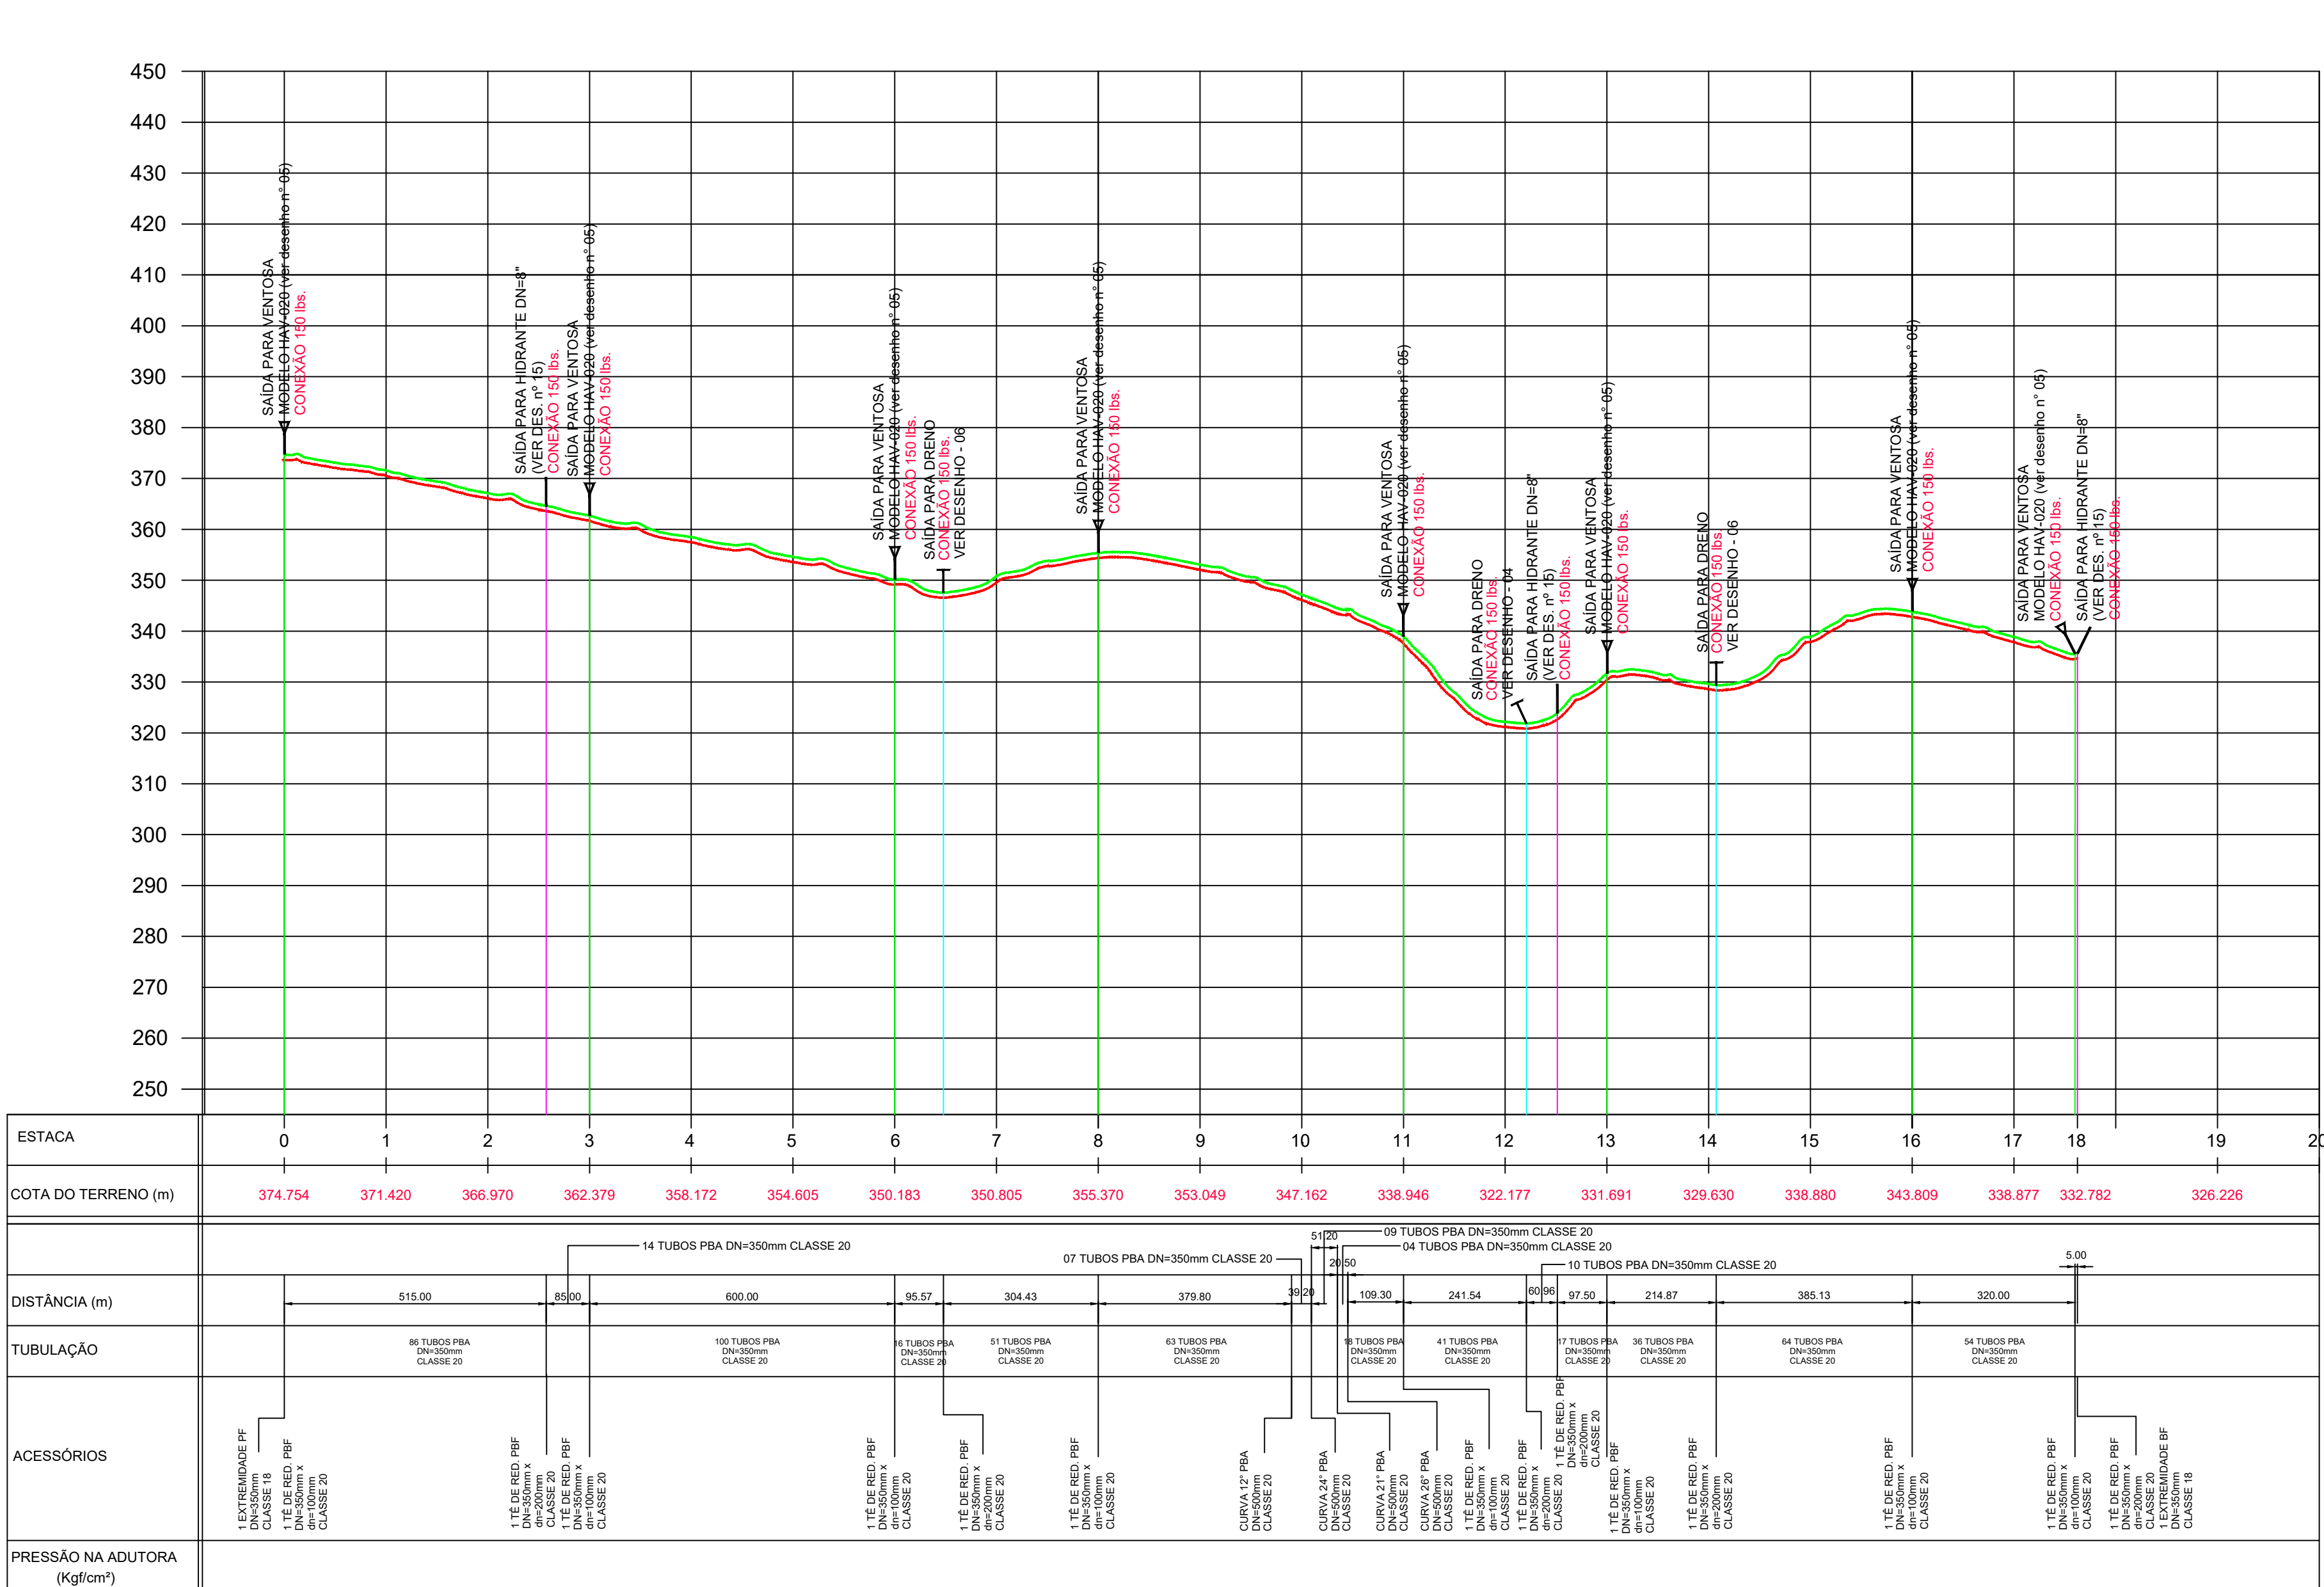


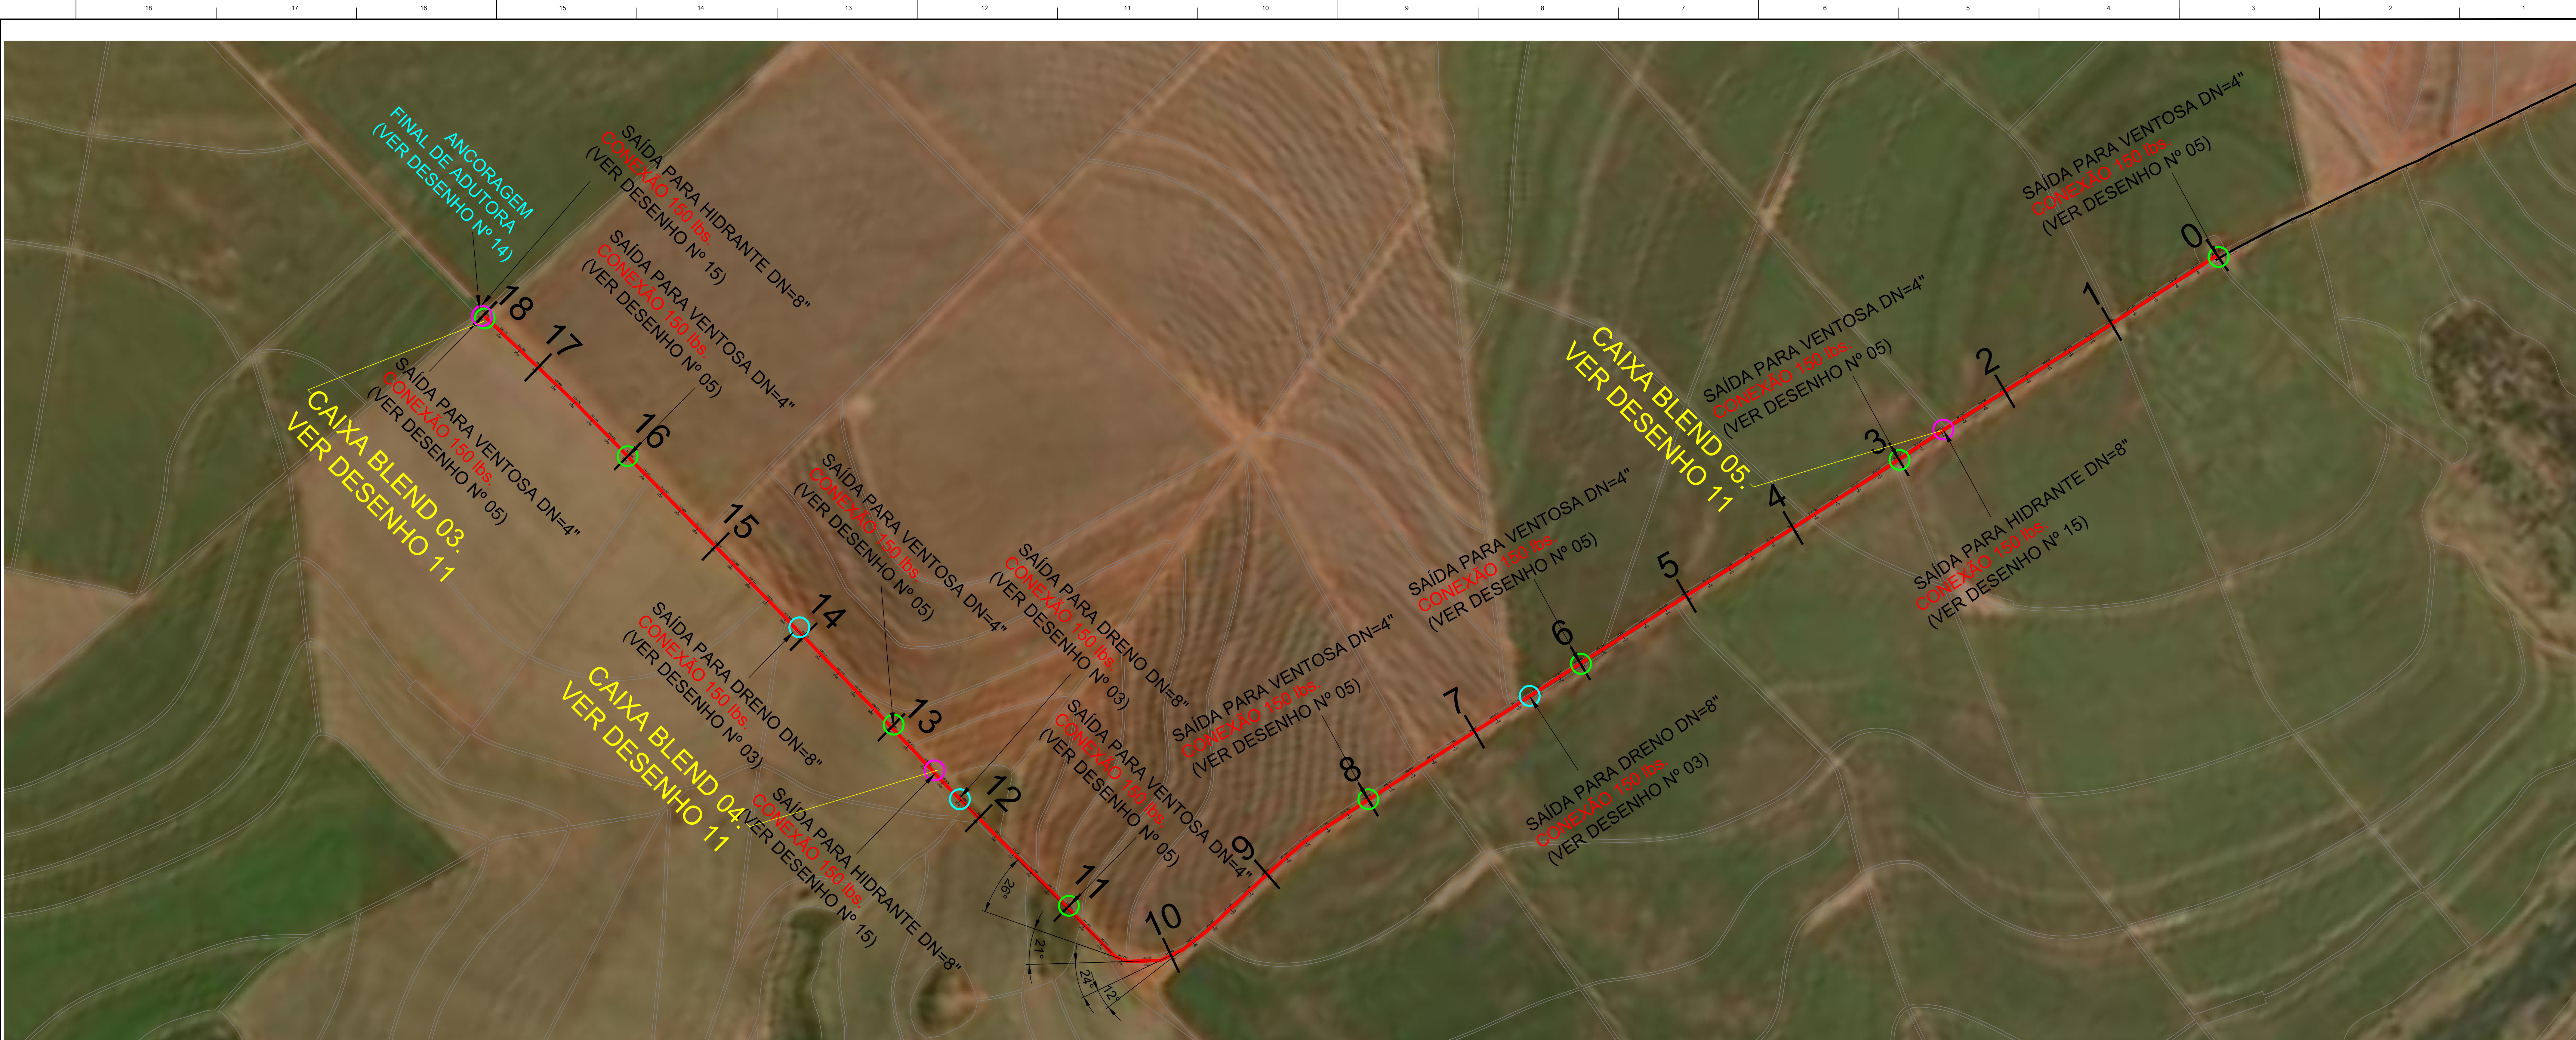

DETALHE BLOCOS DE ANCORAGEM					
UMOE BIOENERGY					
PROJETO DE FERTIRRIGAÇÃO 2025 - AR-RENASCEER					
BLOCOS DE ANCORAGEM NA ADUTORA				DIMENSÕES DO BLOCO (cm)	
PEÇA	ÂNGULO	DIAMETRO ES.TACA	POSICÃO	E (mm)	B C
CURVA	12	350	Entre 10 e 11	Horizontal	150 150 150
CURVA	24	350	Entre 10 e 11	Horizontal	150 150 150
CURVA	21	350	Entre 10 e 11	Horizontal	150 150 150
CURVA	26	350	Entre 10 e 11	Horizontal	150 150 150
VENTOSA	(Ver detalhes e dimensões nos desenhos específicos)				
VALVULAS	(Ver detalhes e dimensões nos desenhos específicos)				
FINAL	(Ver detalhes e dimensões nos desenhos específicos)				
*o bloco deve estar em contato com o diretu natural não escavado, mesmo que seja necessário construí-lo com espessura maior que a INDICADA					

AS TRAVESSIAS DE CARREADOR COM TRÁFEGO, DEVEM SER PROTEGIDAS COM PLACAS DE CONCRETO, VER DESENHO DA VALA, DESENHO 04.

- NOTAS:
- 1) PROJETO ELABORADO COM BASE EM LEVANTAMENTOS TOPOGRÁFICOS FORNECIDOS PELO CLIENTE.
 - 2) HAV-226: VÁLVULA VENTOSA SECA (ESTANCAÇÃO) COMBINADA TRÍPLICE FUNÇÃO, PARA VINHAÇA, CORPO TOTALMENTE EM AÇO INOX. FLUTUADOR INFERIOR EM AÇO INOX, FLUTUADOR SUPERIOR EM POLIPROPILENO EXPANDIDO, JUNTAS EM BUNA-N, VEDAÇÃO DO FLUTUADOR EM EPDM. PRESSÃO DE TRABALHO DE 0,2 A 16,0 KGf/cm². TEMPERATURA ATÉ 60°C. CONEXÃO FLANGEADA DE 3", NORMA ANSI B16.5. MODELO HAV-020 MARCA HIDRO-AMBIENTAL.
 - 3) EM LOCAIS DE TRÁFEGO PESADO E INTENSO, A TUBULAÇÃO DEVERÁ SER PROTEGIDA COM LAJE DE CONCRETO ARMADO CONFORME DES. Nº 04
 - 4) ESQUEMA DA VALA PARA ASSENTAMENTO DA TUBULAÇÃO VER DES. Nº 04
 - 5) FURAÇÃO DOS FLANGES DE RPVC SEGUE A NORMA ANSI B16.5.

LISTA DE MATERIAL DA ADUTORA - SERGIPE

QTD	DESCRIÇÃO	ESPECIFICAÇÃO	UNID.	QTD	DESCRIÇÃO	ESPECIFICAÇÃO	UNID.
07	01	CURVA 26" PBA DN=350mm CLASSE 20	RIGIDEZ 3750N/m ²	RPVC	60°C		
06	01	CURVA 21" PBA DN=350mm CLASSE 20	RIGIDEZ 3750N/m ²	RPVC	60°C		
05	01	CURVA 24" PBA DN=350mm CLASSE 20	RIGIDEZ 3750N/m ²	RPVC	60°C		
04	01	CURVA 12" PBA DN=350mm CLASSE 20	RIGIDEZ 3750N/m ²	RPVC	60°C		
03	06	TE DE RED. PBF. DN=350 x Ø=200mm, CLASSE 20	FURAÇÃO 150 lbs.	RPVC	60°C		
02	06	TE DE RED. PBF. DN=350 x Ø=100mm, CLASSE 20	FURAÇÃO 150 lbs.	RPVC	60°C		
01	595	TUBO PBA, DN= 350mm, CLASSE 20, BARRA 6m	RIGIDEZ 3.750N/m ²	RPVC	60°C		
POS.	QUANT.			MATERIAL	QUALIDADE		

Nº Rev.	Data	Modificação	Revisor	Aprovação
DESENHO TIPO:	☐ PRELIMINAR	☒ P1 APROVAÇÃO	DESENHO:	☐ APROVADO
	☐ P1 REFERÊNCIA	☐ CERTIFICADO		☐ NÃO APROVADO
17/07/2025	DATA:	RESPONSÁVEL:	DATA:	RESPONSÁVEL:
VERONEZ PROJETOS E CONSULTORIA				
CLIENTE: UMOE BIOENERGY				
LOCAL: SANDOVALINA - SP		RESP. TÉCNICO: Eng. Sérgio Antônio Nogueira de Sousa		DATA:
DENOMINAÇÃO: PROJETO DE FERTIRRIGAÇÃO - 2025		ESCALA: 1:10.000		VEREDICTO:
ADUTORA DE RECALQUE - AR-AGUA MANSA		NÚMERO: SV-UMOE-PE		
PLANTA E PERFIL		2501-12		0